


МТМ 1565.00.00.000 СБ

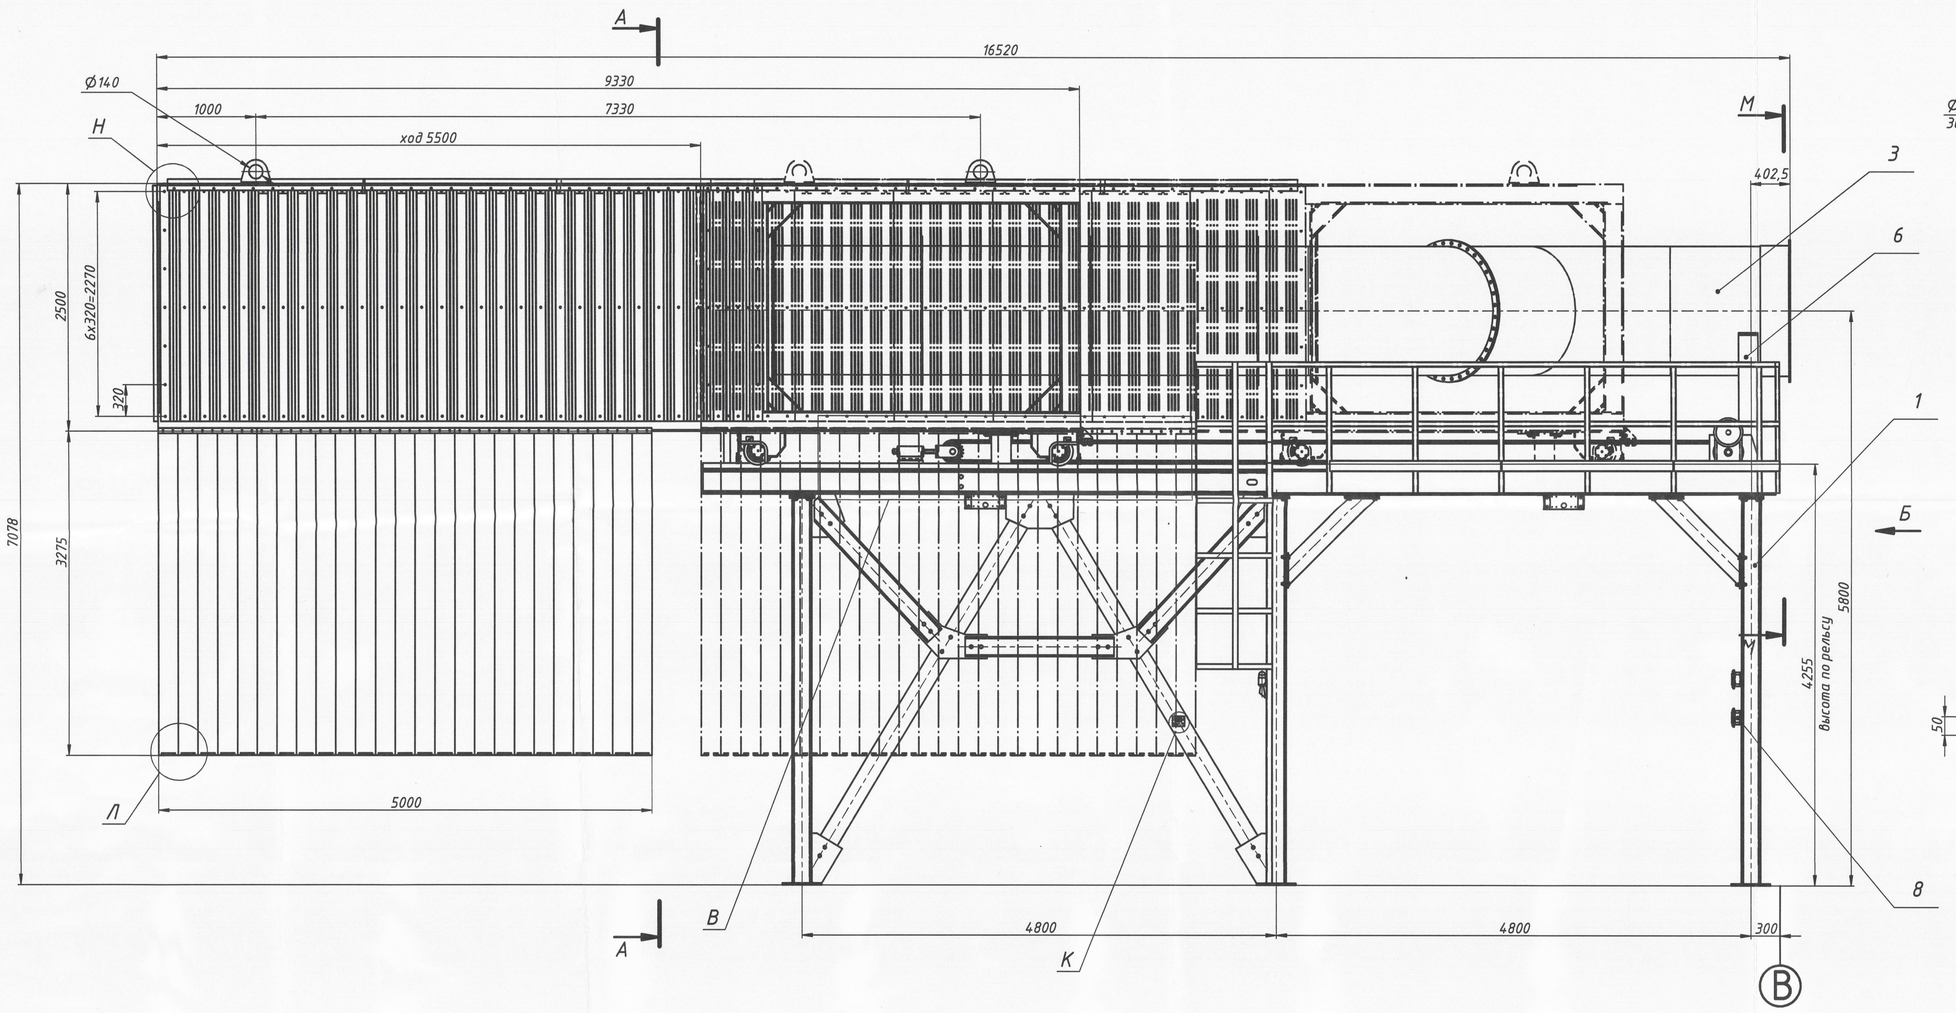


М–М (1 : 20)

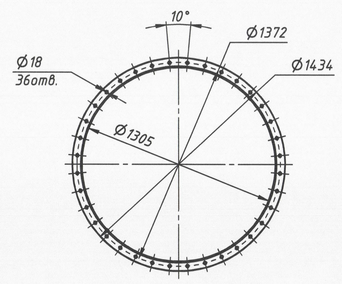


Л (1 : 10)

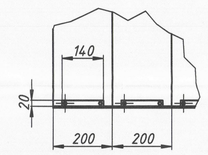


Н (1 : 8)

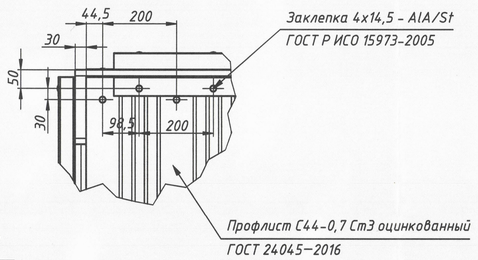


А–А (1 : 30)

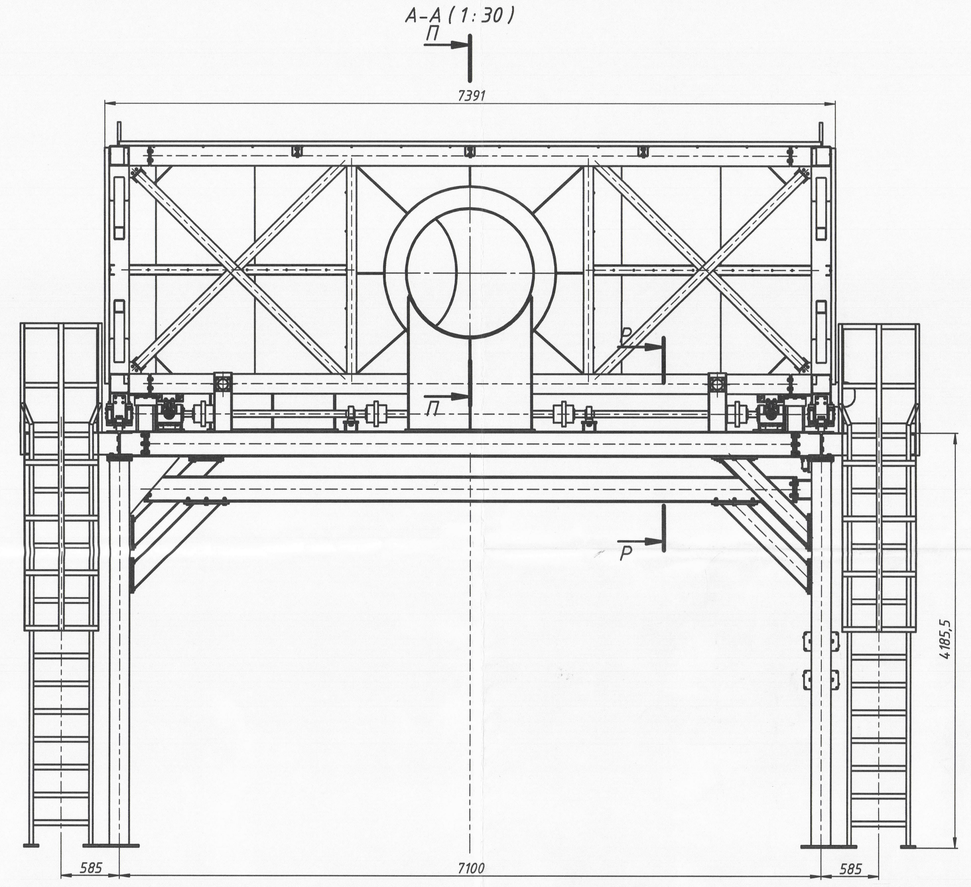


Б (1 : 30)

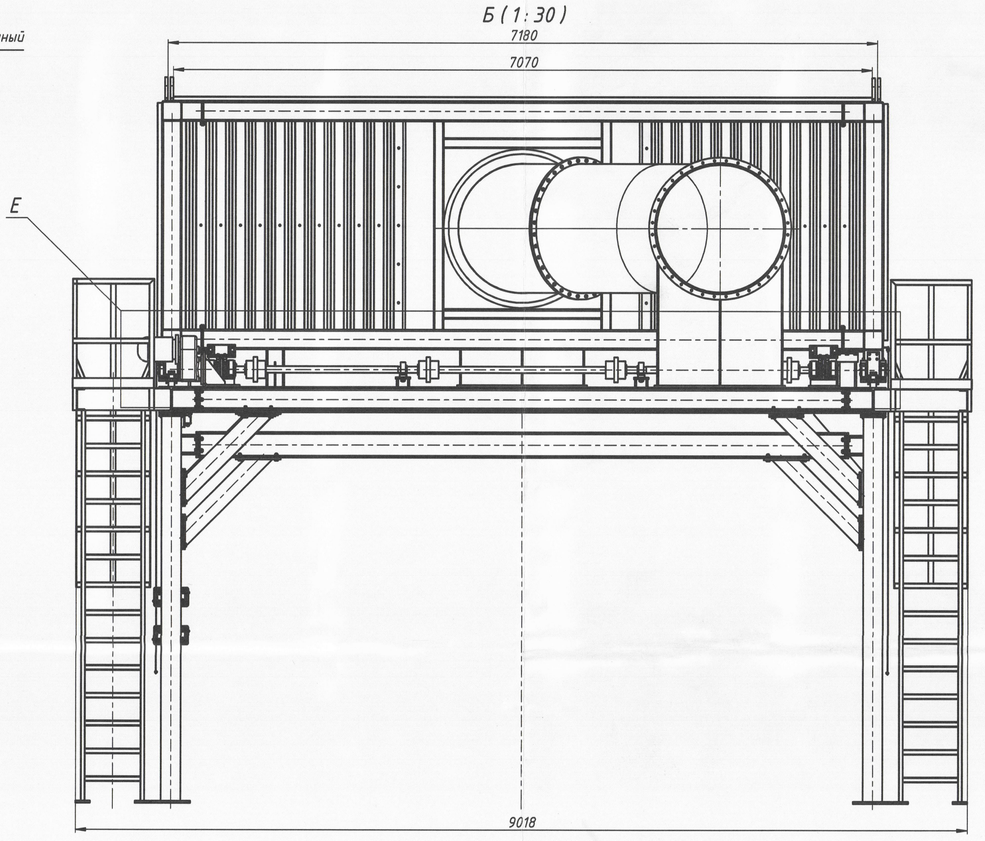


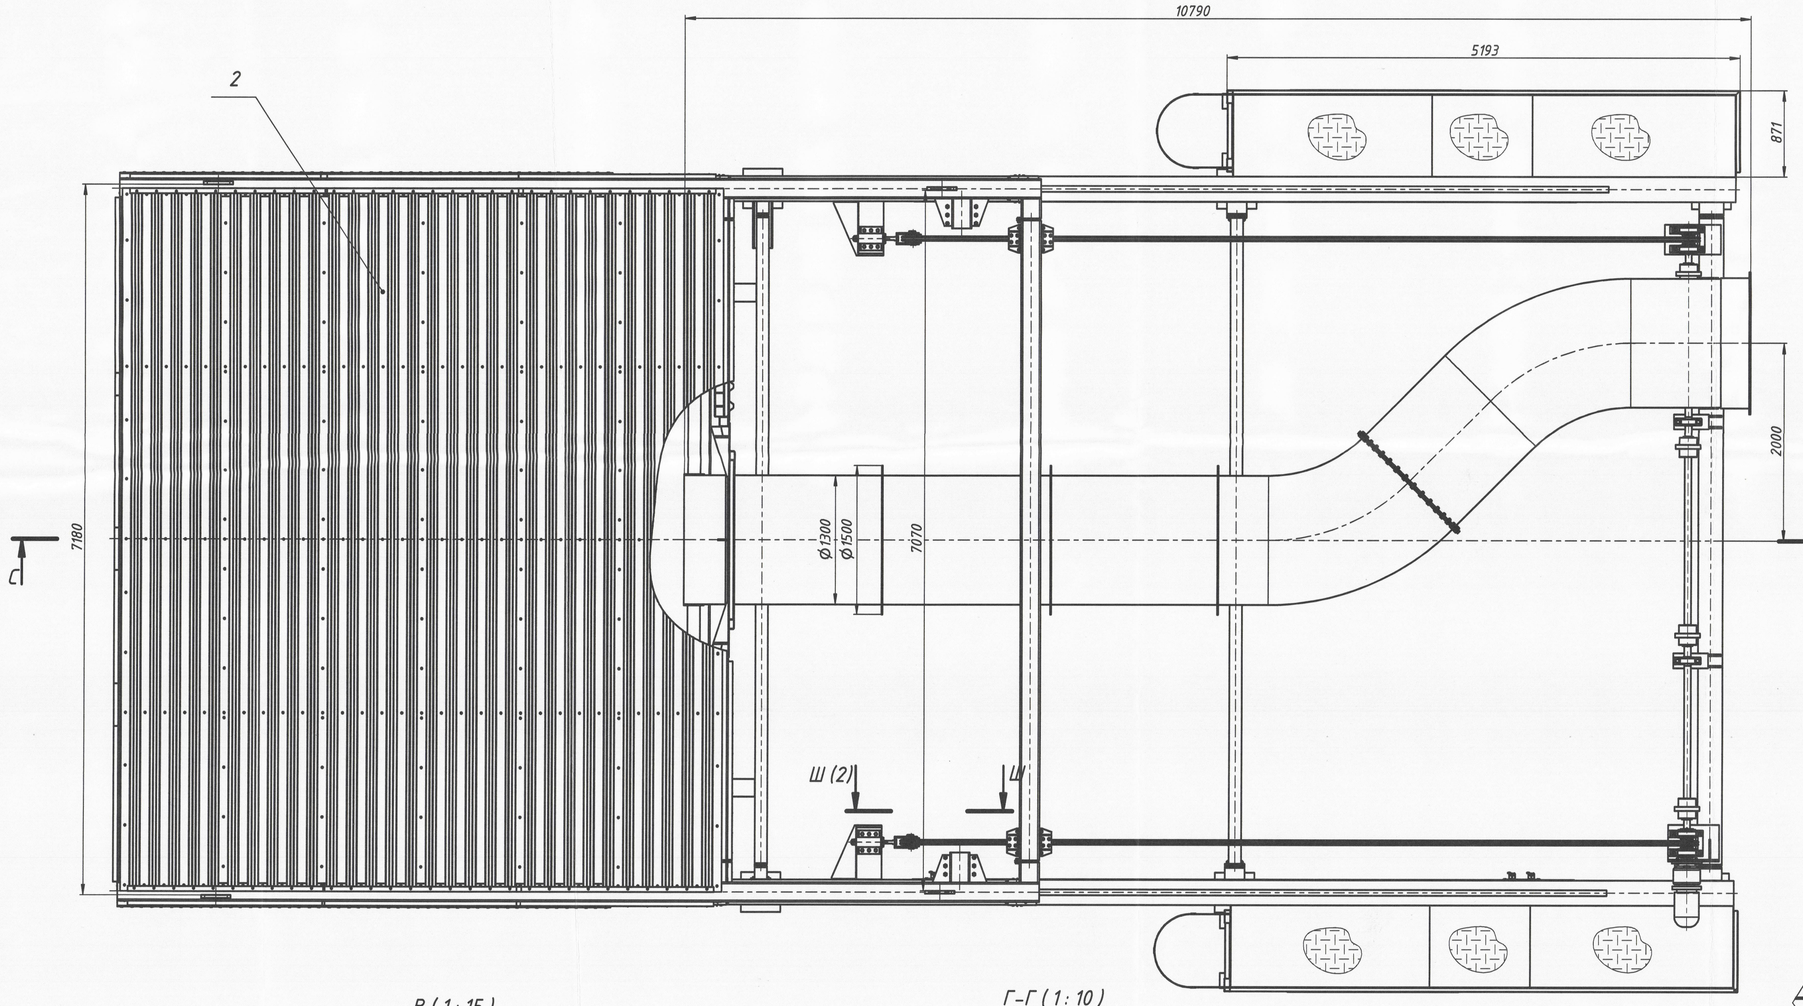


П–П (1 : 15)

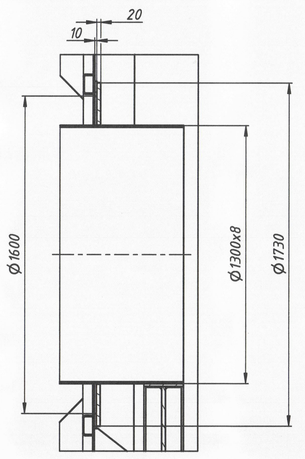


И (1 : 8)

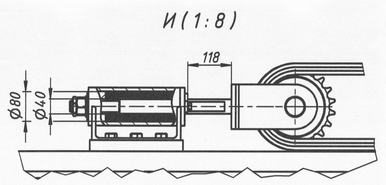

Ж (1 : 8)

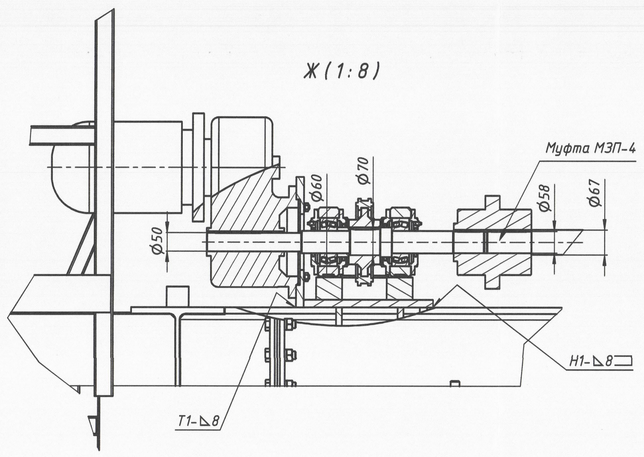


Р–Р (1 : 15)

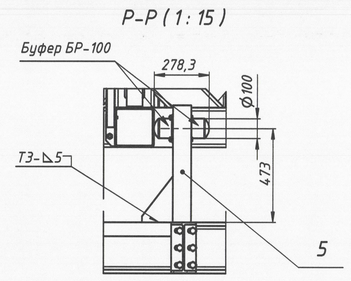


К (1 : 4)




Е (1 : 25)

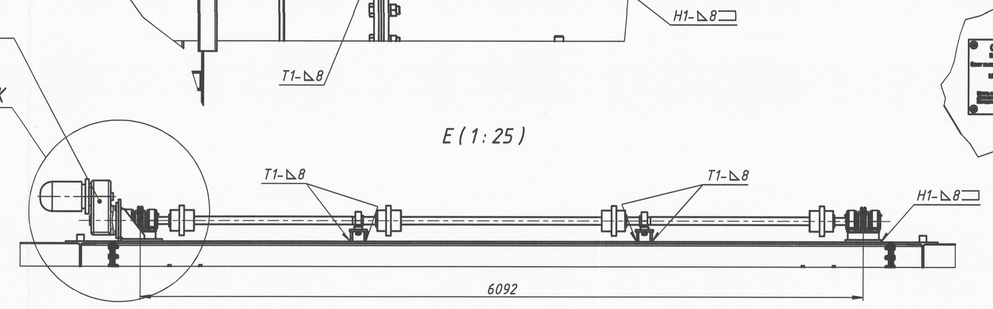


В (1 : 15)

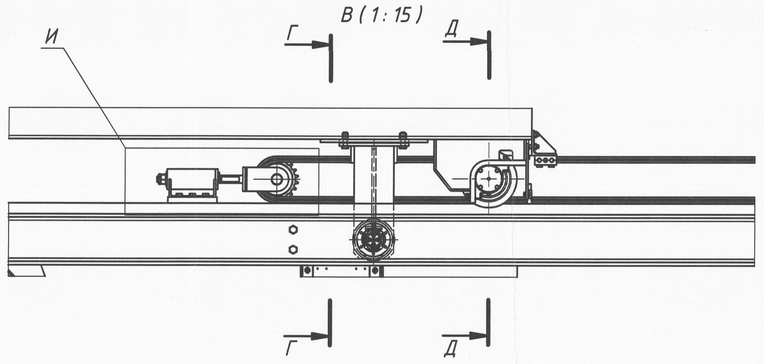

Г–Г (1 : 10)

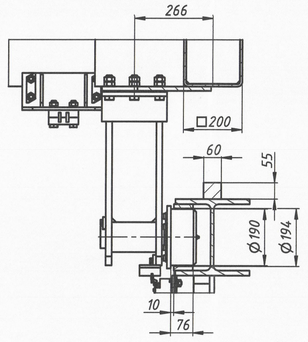

Д–Д (1 : 10)

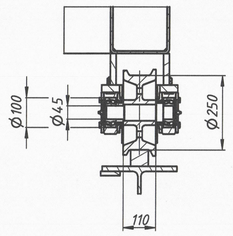

ТЕХНИЧЕСКИЕ ХАРАКТЕРИСТИКИ

1. Привод зонта цепной – Цепь ПР–31,75–89
2. Мотор–редуктор со встроеным тормозом "Европривод" FAF77.85,52.16.1,5х1400.М1.270 (2,2кВт, 16об/мин, SFном–1,2) – 1шт.
3. Скорость перемещения зонта – 10м/мин.
4. Масса подвижной части зонта – 8395кг.
5. Материал штор – Арселоновая ткань 300г/м2 (t=250°)
6. Управление перемещением зонта – стационарный пульт управления (не входит в поставку ООО "МТМ").
7. Зонт и рама поставляются в разобранном виде укрупненными частями с последующей сборкой на месте эксплуатации силами заказчика.

ТЕХНИЧЕСКИЕ ТРЕБОВАНИЯ

1. Чертеж выполнен на основе чертежа DPC13Y–GS51–B2000–AD013.
2. Все размеры справочные.
3. Сборку зонта выполнять в соответствии с чертежами: МТМ1565.01.00.000 МТМ1565.02.01.000 МТМ1565.02.02.000 МТМ1565.02.03.000 МТМ1565.02.04.000 МТМ1565.02.05.000 МТМ1565.02.00.000 МТМ1565.03.00.000 МТМ1565.04.00.000 МТМ1565.05.00.000 МТМ1565.06.00.000 МТМ1565.07.00.000 МТМ1565.50.00.000
4. Общие допуски по ГОСТ 30893.1 – т.
5. После изготовления выполнить контрольную сборку, замеры и функциональные испытания.
6. Установку, приварку и регулировку конечных выключателей выполнить после сборки зонта на месте эсплуатации.
7. Упоры поз.5 установить и отрегулировать пластинами на месте эксплуатации после сборки зонта.
8. Клемную коробку и светозвуковой сигнал установить и приварить после сборки зонта на месте эксплуатации.
9. Перед первым пуском необходимо заправить редуктор согласно паспорту изделия.
10. После сборки на месте эксплуатации строповочные проушины на зонте допускается срезать.
11. Нарушенное покрытие восстановить эмаль ОС–51–03 ТУ84–725–78 серый.
12. Покрытие–эмаль ОС–51–03 ТУ84–725–78 серый ; лак КО–921 ГОСТ16508–70.

				МТМ 1565.00.00.000 СБ		
Изм.	Лист	№ докум.	Подп.	Дата		
Разраб.		Сумонов АС			Зонт вытяжной установки скачивания шлака	Лит.	Масса	Масштаб
Пров.							21620	1:30
Т. контр.		Зайка ПИ				Лист 1	Листов 3	
Н. контр.						ООО "МТМ"		
Утв.		Карповдв						

Копировал Формат А0

Инв.№ подл. | Подп. и дата | Взам. инв.№ | Инв.№ дубл. | Подп. и дата